朝里川温泉Ｂｖ Ｐ１橋脚 構造一般図（その１） S=1/200

側 面 図 S=1/200

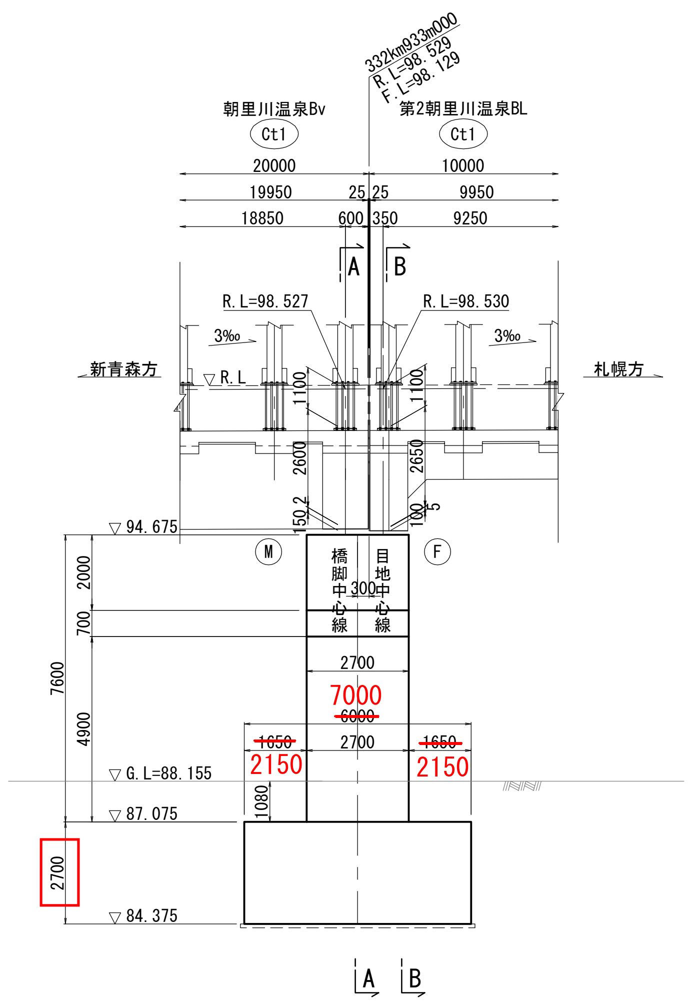

正 面 図 S=1/200

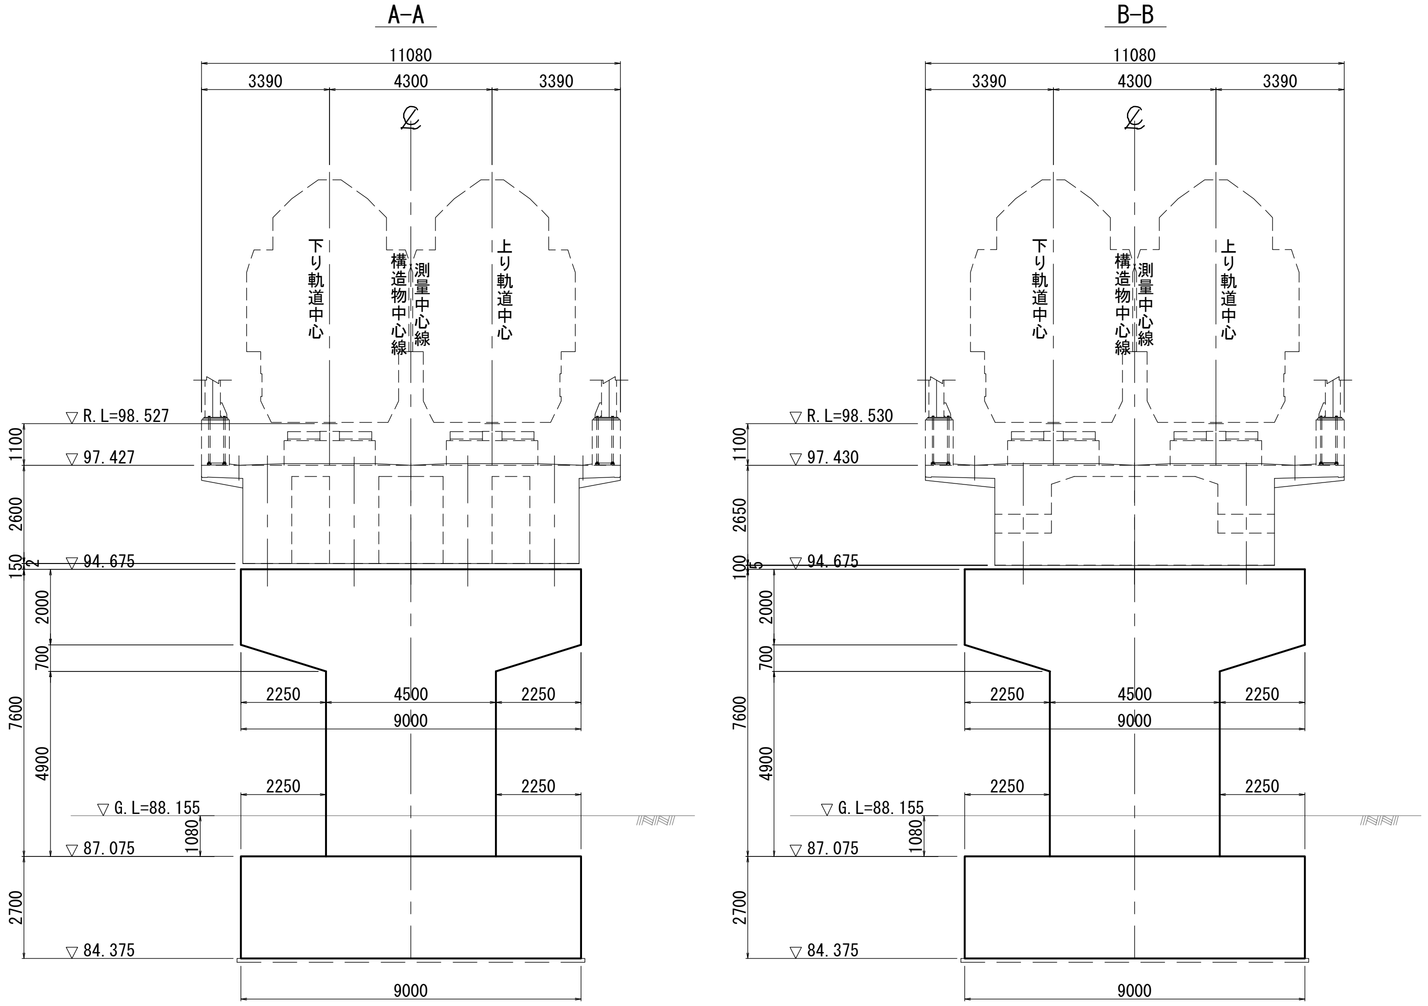

基礎平面図 S=1/200

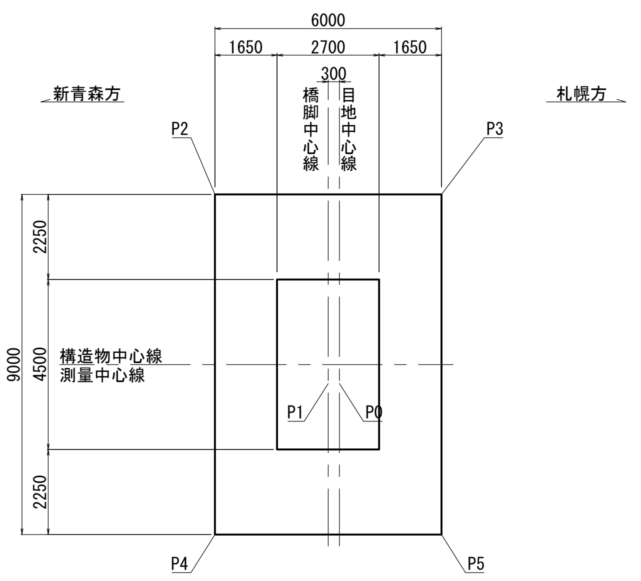

桁座詳細図 S=1/100

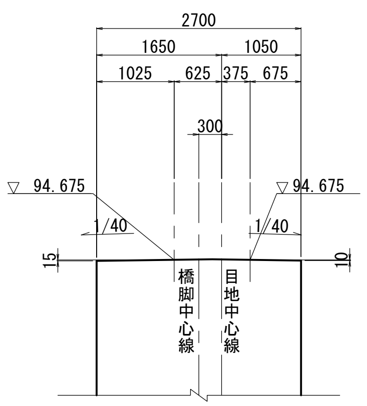

基礎座標値

	X	Y
P0		
P1		
P2		
P3		
P4		
P5		

注1）P0は測量中心線と目地中心線の交点

注2）P1は橋脚の構造中心点

設 計 条 件

線　　名		北海道新幹線（新青森～札幌間）		
構造形式		複線用壁式橋脚（直接基礎）		
前後の支間長（桁種別）		起点側： 20m 可動（RCT形桁） 終点側： 10m 固定（RCT形桁）		
橋脚の高さ		フーチング天端 ～ シュー座面 7.600m		
設計列車荷重 設計速度		標準列車荷重 P-16 , V=320km/h		
曲線半径、設計ｶﾝﾄ		直線		
斜　　角		90 度		
線路縦断勾配		上り 3 ‰		
軌道種別		スラブ軌道		
設計耐用期間		100 年		
設計想定地震動と耐震性能		Ｌ１地震動		走行安全性
		Ｌ２地震動		安全性
		復旧性検討地震動（スペクトルⅡ）		復旧性
		地域別係数		0.7（後志支庁）
		計算された地盤区分		Ｇ２地盤
構造物の環境条件		躯　体・桁受け梁（上面）		腐食性環境
		フーチング・桁受け梁（下面）		一般の環境
鉄筋のかぶり（寒冷地）		躯　体・桁受け梁	フーチング	
		70mm以上	50mm以上 100mm以上（下側水平鉄筋）	
コンクリートの品質	部　材	躯　体	桁受け梁	フーチング
	設計基準強度	27 N/mm²	27 N/mm²	27 N/mm²
	セメントの種類	普　通	普　通	高炉（Ｂ）
	骨材の種類	普　通	普　通	普　通
	粗骨材の最大寸法	25 mm	25 mm	40 mm
	スランプの範囲	8±2.5cm	12±2.5cm	8±2.5cm
	空気量の範囲	5.5±1.5%	5.5±1.5%	4.5±1.5%
	最大水セメント比	53 %	53 %	55 %
	単位水量の上限値	175 kg/m³	175 kg/m³	165 kg/m³
鉄筋の品質	部　材	躯体・桁受け梁・フーチング		
	種　別	SD390		
	設計引張強度	560 N/mm²		
	設計引張降伏強度	390 N/mm²		
適用設計標準		コンクリート（H16.4）	基礎（H24.1）	耐震（H24.9）

施工上の注意事項

１．バイブレーターは主鉄筋のかぶりの部分に確実に掛けること。

２．養生は型枠をはずした後も継続し、所定の期間の湿潤養生を行い、ひび割れ防止に努めること。

３．ストッパー用の箱抜きやシュー座の箱抜きには、雨水が溜まらないように水抜きを設けるあるいはカバーをすること。

４．諸設備用のアンカーボルト、インサート金具および埋込栓等は、監督員と打合せの上できるだけ後施工とならないよう設置すること。

５．桁座には１／４０以上の排水勾配を設けること。

６．シュー座モルタル、ゴムシューは上部工工事とする。

７．高さ表示は、すべてＴ．Ｐ表示である。

設計番号	＊＊＊＊ＯＯＯ—ＯＯＯＯＯ						
契約番号	道建役３０第４４号 北海道新幹線、新小樽（仮称）駅高架橋外1箇所詳細設計他						
主任技術者	栗山　亮介			照査技術者	大野　恭司		
主査	ｳｫﾝ ｲｴﾝｽｲ	設計	小西亮太	製図	ﾎｼｰ ｸｫｯｸ	照査	花島純郎
設計会社	株式会社　復建エンジニヤリング						
令和 ２ 年 １１ 月							

件　名							
図面名称	朝里川温泉Ｂｖ Ｐ１橋脚 構造一般図（その１）						
縮　尺	1/200			図面番号	葉の内		
課長		課長補佐		担当係長		設計	
独立行政法人 鉄道建設・運輸施設整備支援機構 北海道新幹線建設局				令和　年　月			

００００００—０００＊＊＊＊

朝里川温泉Ｂｖ Ｐ１橋脚 構造一般図（その２）

支承部詳細図 S=1/100

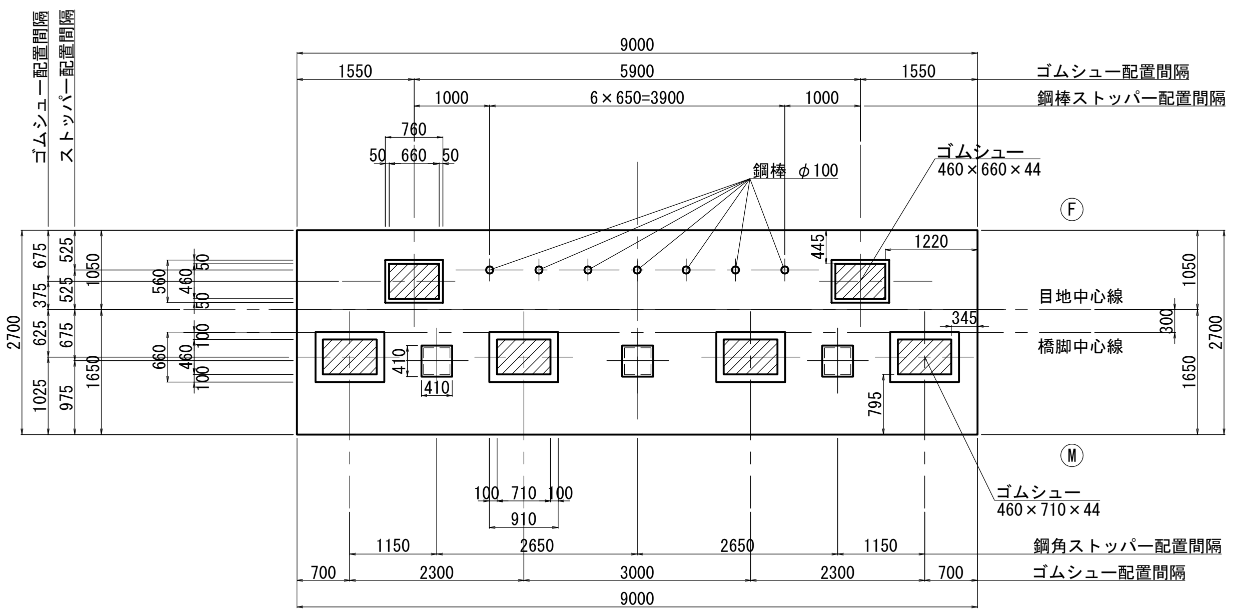

地質柱状図 S=1/300

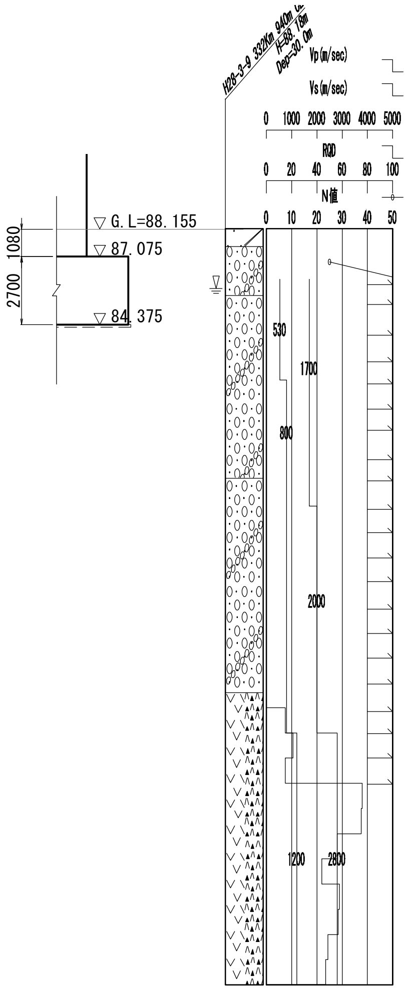

区分	層厚 (m)	N値	γ (kN/m³)	Vs (m/s)	Ed (kN/m²)
B	0.70	—	18.00	170	15560
Al1-1	1.95	31	18.00	700	42710
Al1-2	3.35	90	19.00	1700	165760
Al1-3	3.90	151	19.00	2000	367010
Al2	8.50	146	19.00	2000	367010
Umt(Hy)	11.60	195	21.00	2800	856590

設計番号	＊＊＊＊０００—０００００		
契約番号	道建役３０第４４号 北海道新幹線、新小樽（仮称）駅高架橋外1箇所詳細設計他		
主任技術者	栗山 亮介	照査技術者	大野 恭司

主査	ｳｫﾝ ｲｴﾝｽｲ	設計	小西亮太	製図	ﾎｼｰ ｸｫｯｸ	照査	花島純郎
設計会社	株式会社 復建エンジニヤリング						
令和 ２ 年 １１ 月							

件名			
図面名称	朝里川温泉Ｂｖ Ｐ１橋脚 構造一般図（その１）		
縮尺	1/200	図面番号	葉の内

課長		課長補佐		担当係長		設計	

独立行政法人 鉄道建設・運輸施設整備支援機構 北海道新幹線建設局	令和 年 月

＊＊＊＊０００—０００００